




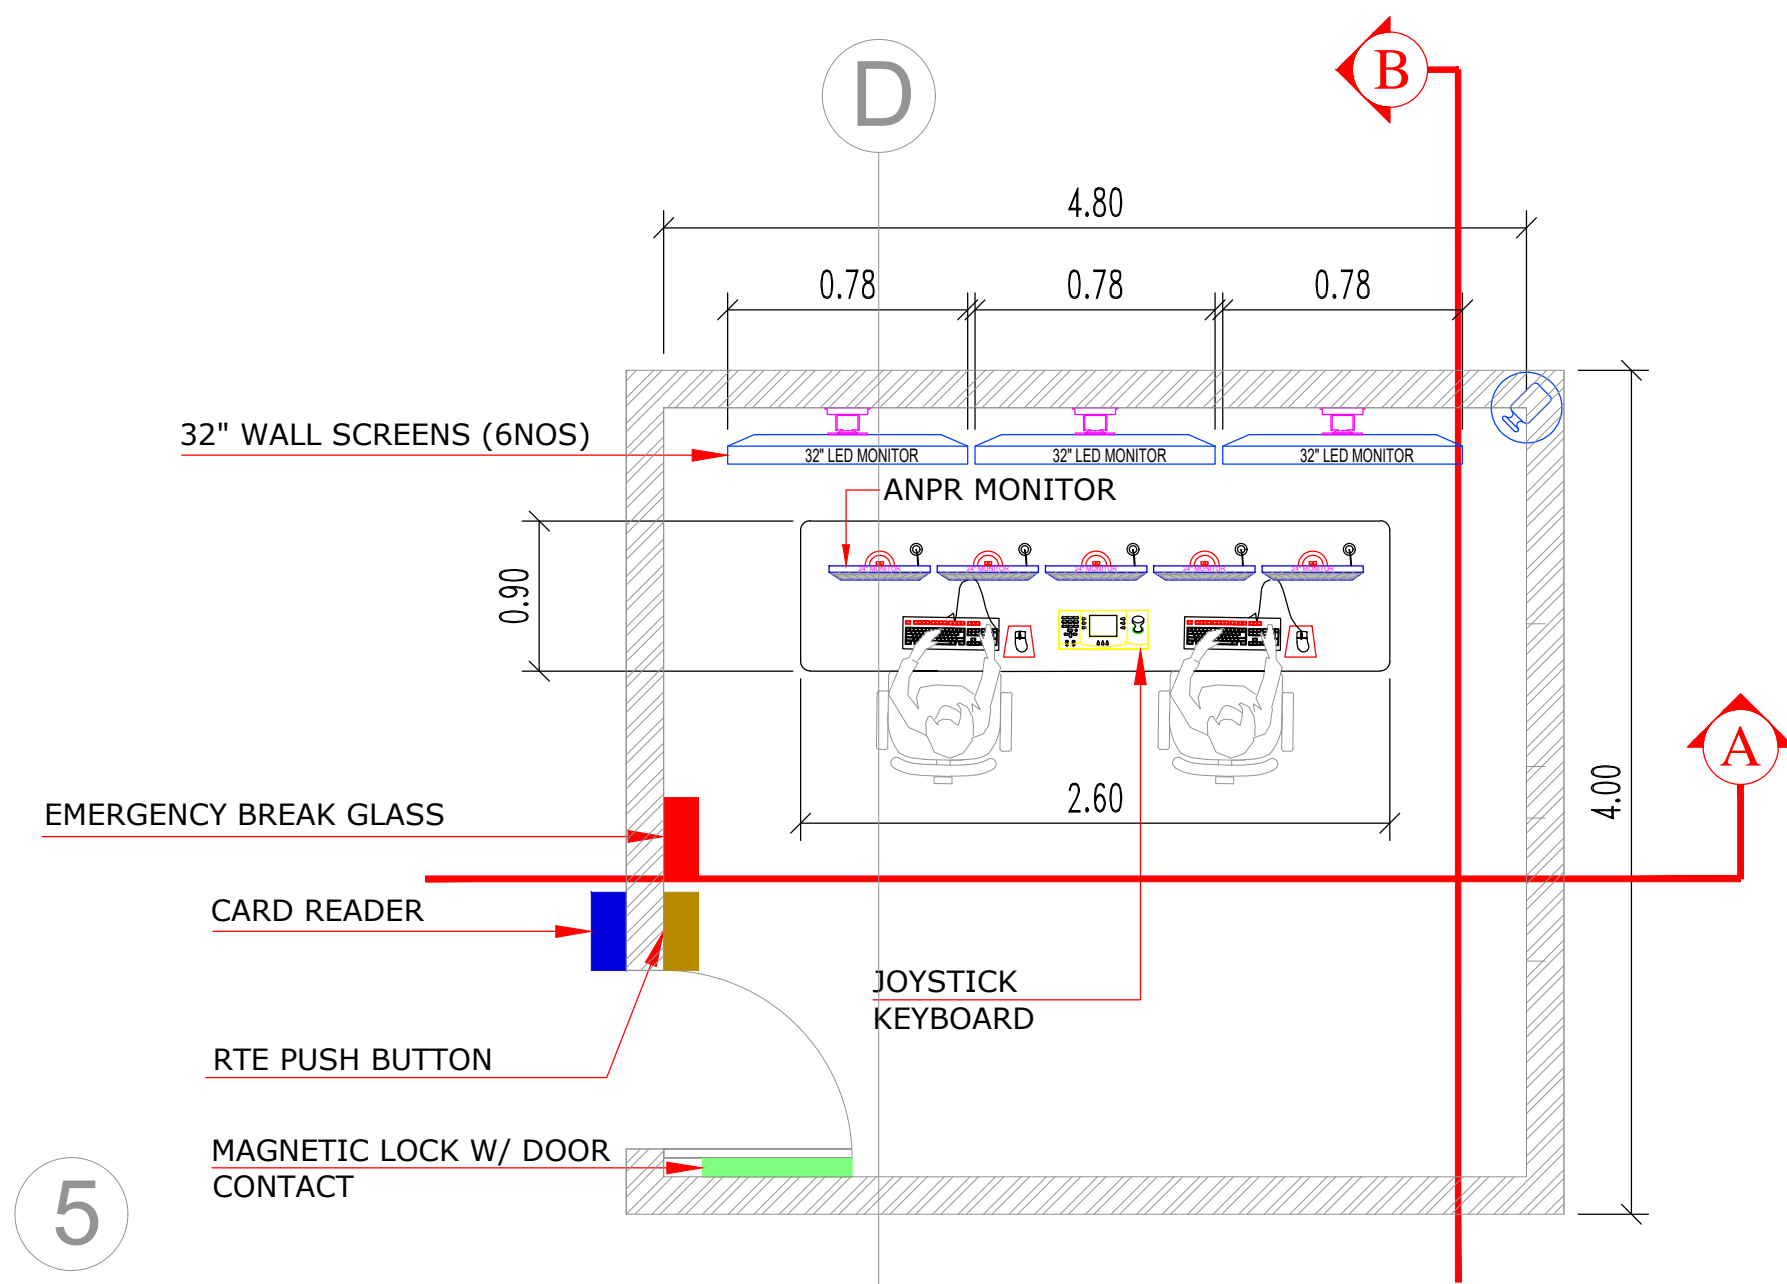


CONTROL ROOM FLOOR PLAN
LOCATED AT SITE PLAN LAYOUT
SCALE 1:25

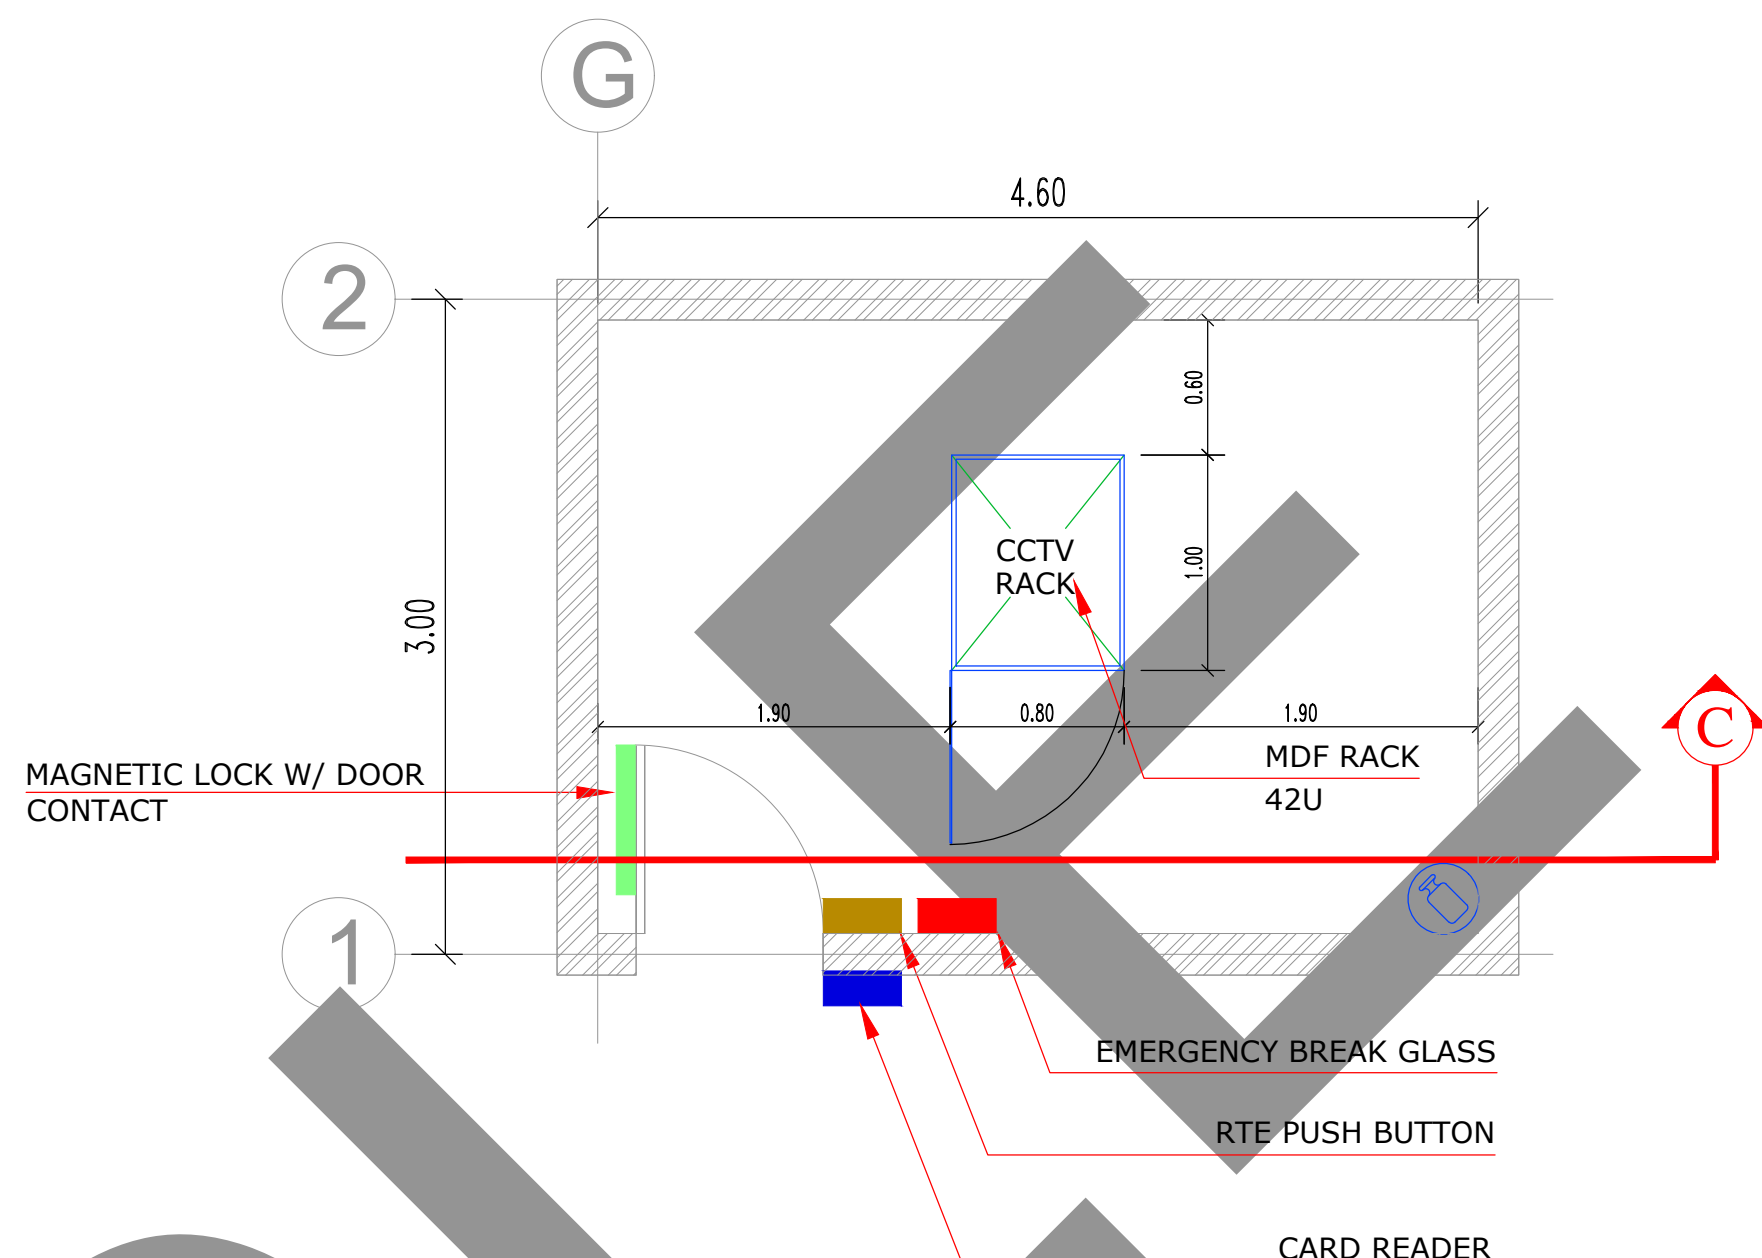


CCTV EQUIPMENT ROOM
LOCATED AT SERVICE BUILDING GROUND FLOOR
SCALE 1:25

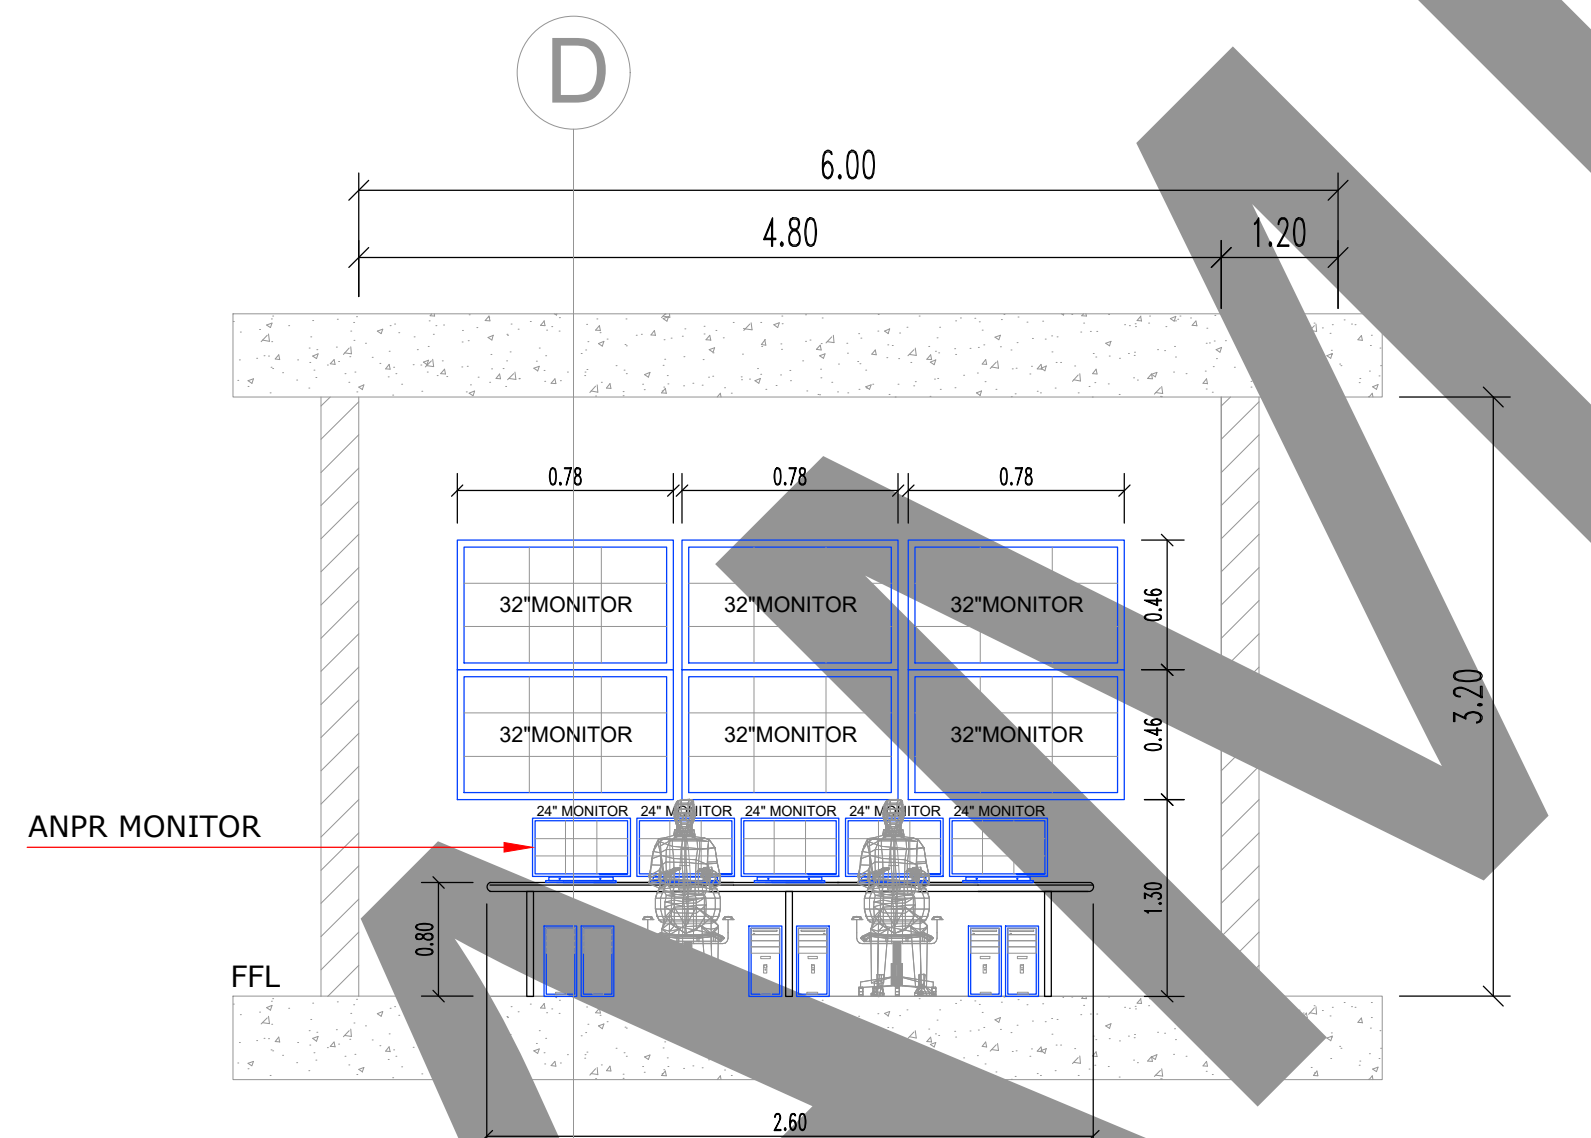


SECTION A-A (FRONT VIEW)
SCALE 1:25

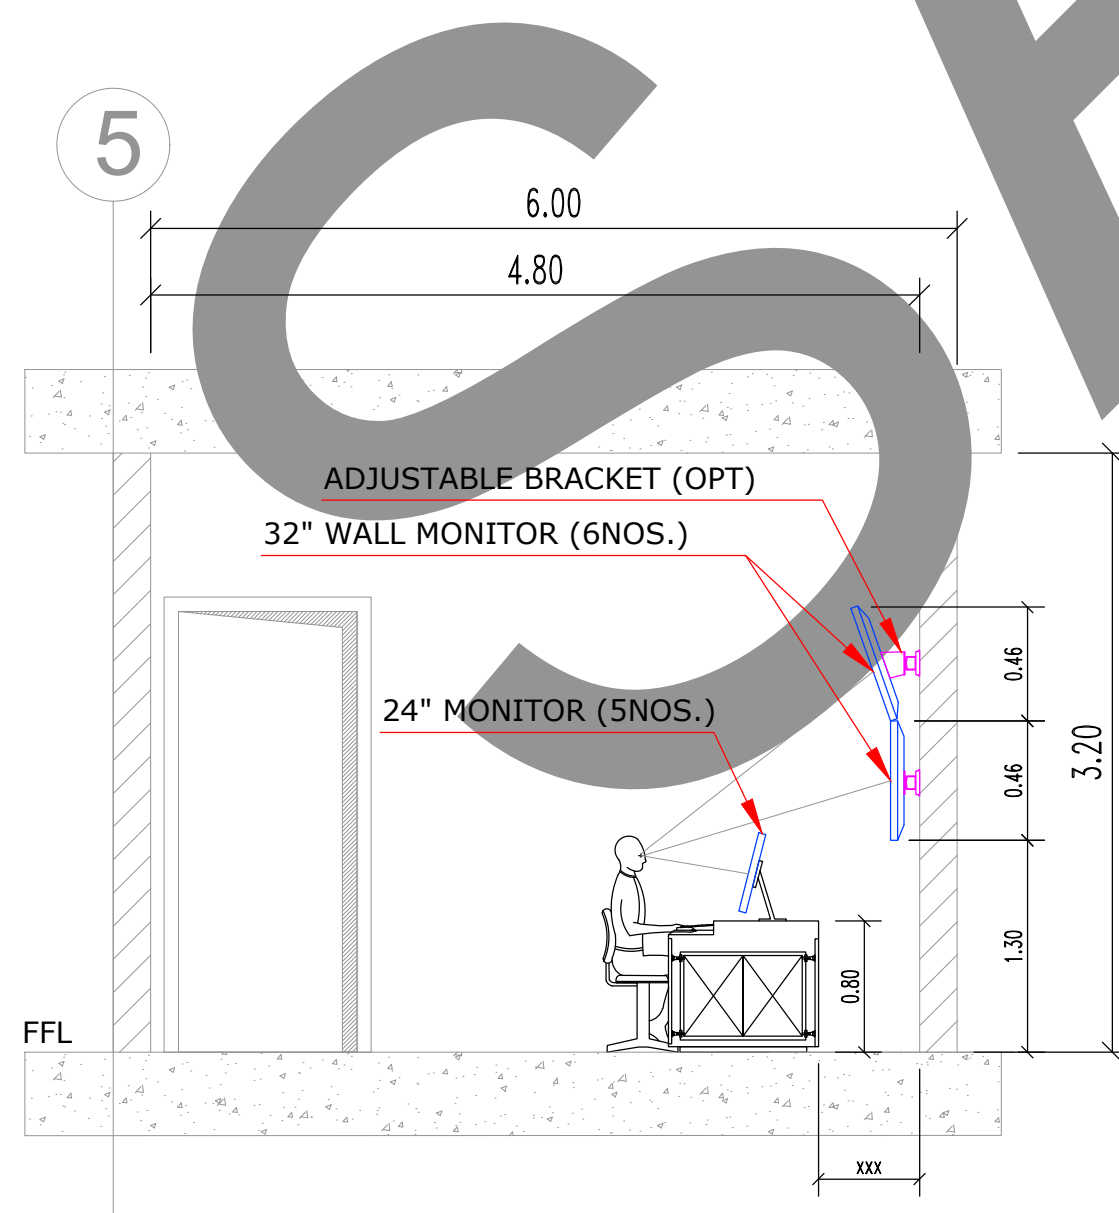

SECTION B-B (SIDE VIEW)
SCALE 1:25

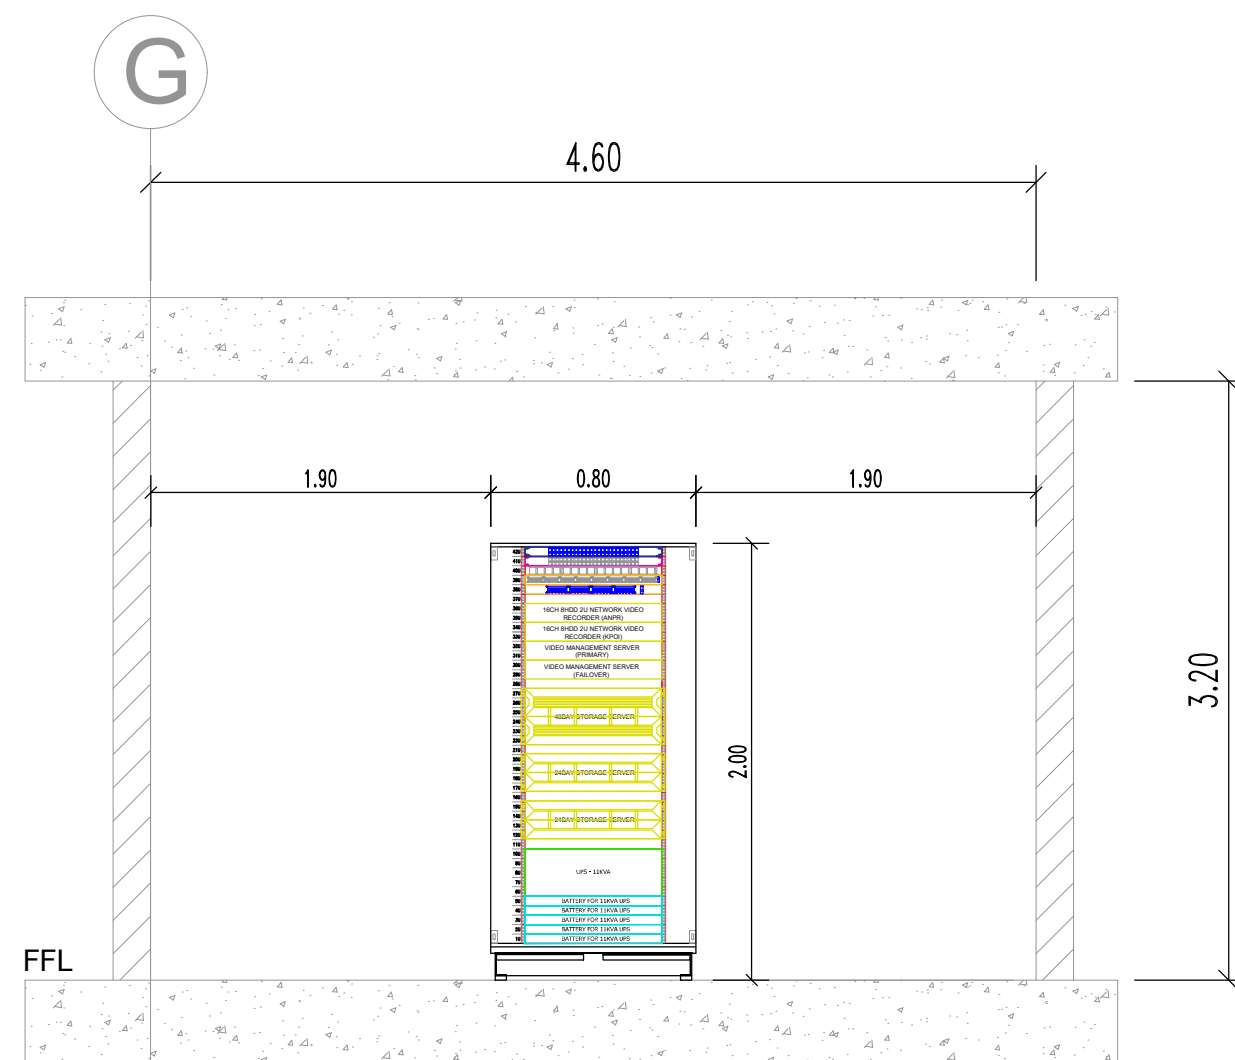



SECTION C-C (FRONT VIEW)
SCALE 1:25

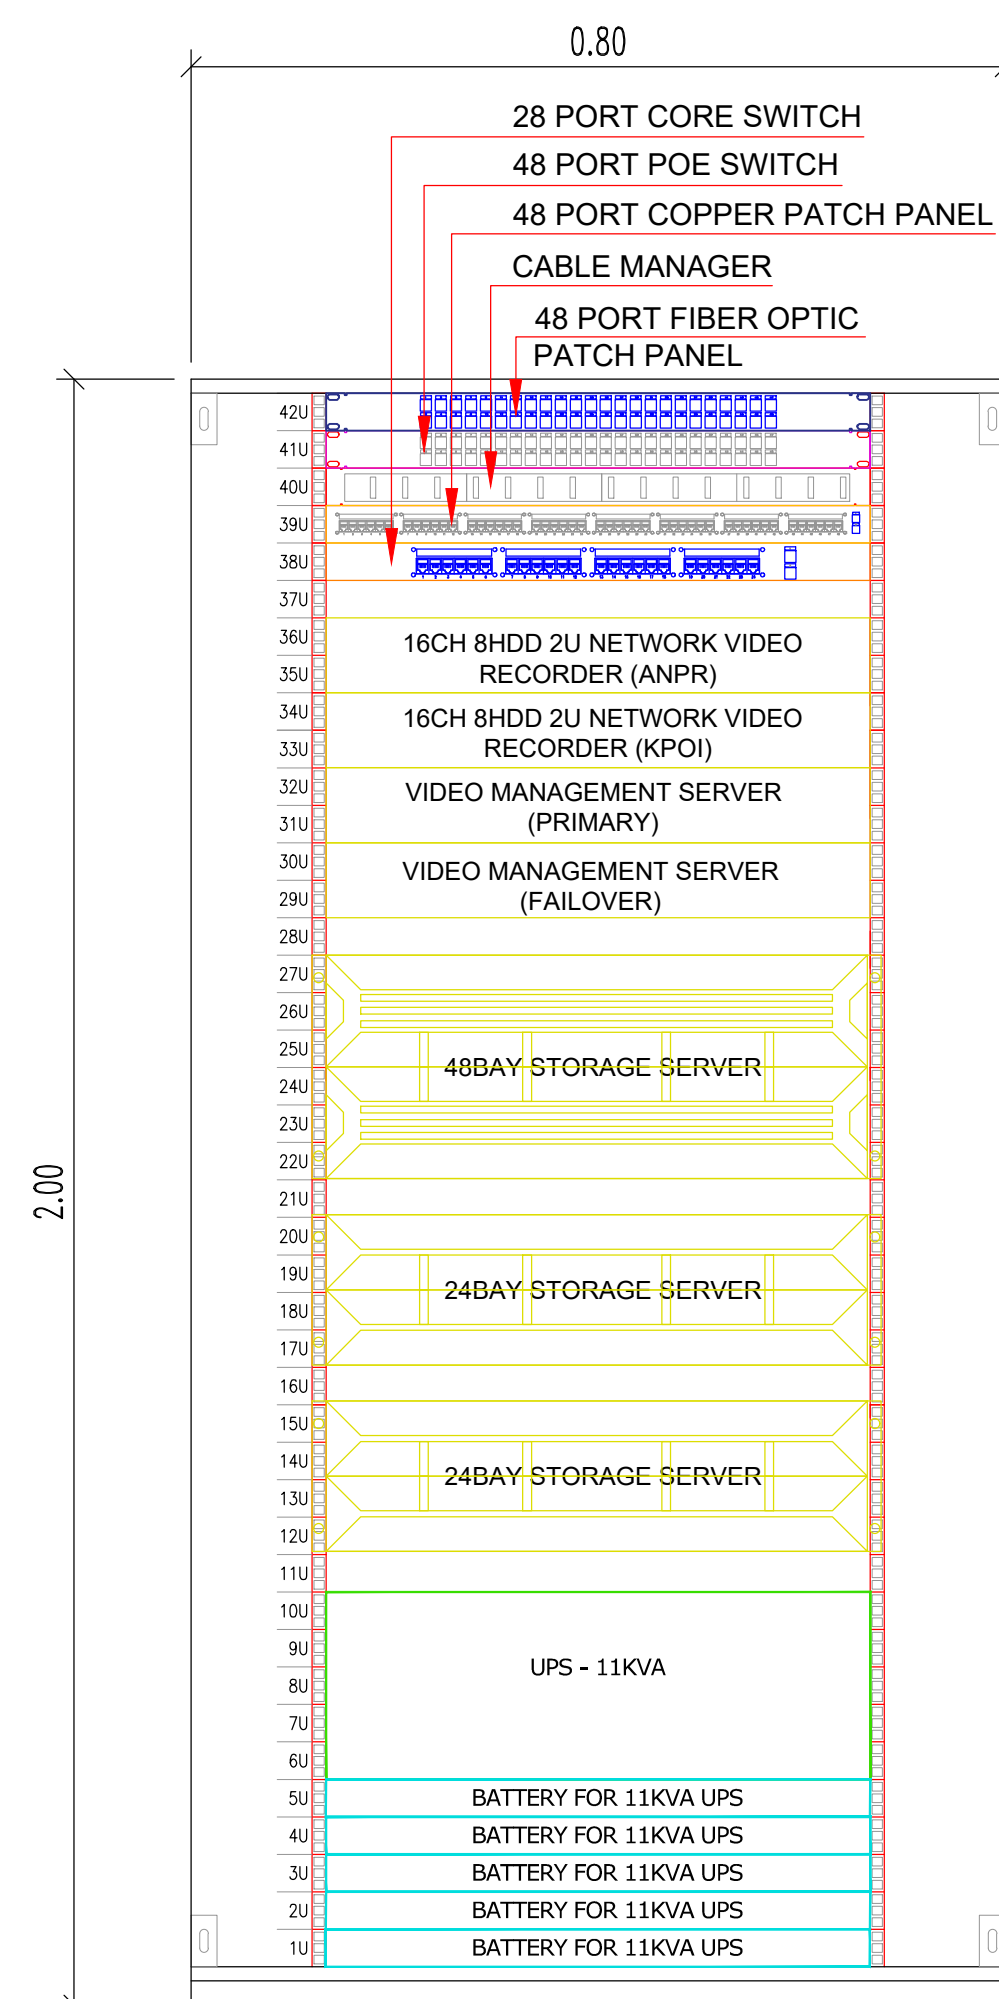

MAIN EQUIPMENT RACK (MDF) - 42U
DETAILED VIEW

CONTROL ROOM & EQUIPMENT ROOM
DEVICE DETAILS:

SYMBOL	DESCRIPTION	QTY.
	2MP VERIFOCAI DOME CAMERA Brand: _____ Model: _____	2
	48-bay EMBEDDED VIDEO STORAGE Brand: _____ Model: _____	1
	24-bay EMBEDDED VIDEO STORAGE Brand: _____ Model: _____	2
	CCTV WORKSTATIONS FOR ANPR Brand: _____ Model: _____	1
	24 INCH MONITOR FOR ANPR Brand: _____ Model: _____	1
	16CH, 8BAY NVR FOR ANPR Brand: _____ Model: _____	1
	16CH, 8BAY NVR FOR KPOI Brand: _____ Model: _____	1
	42 INCH MONITOR FOR ANPR Brand: _____ Model: _____	6
	24 INCH MONITOR FOR ANPR Brand: _____ Model: _____	4
	CCTV WORKSTATIONS Brand: _____ Model: _____	5
	JOYSTICK CONTROLLER Brand: _____ Model: _____	1
	VIDEO MANAGEMENT SEVER Brand: _____ Model: _____	2
	48 PORT POE SWITCH Brand: _____ Model: _____	10
	CORE SWITCH 24 PORT Brand: _____ Model: _____	1
	8 PORT FIBER PATCH PANEL Brand: _____ Model: _____	8
	FIBER PATCH PANEL 48 PORT Brand: _____ Model: _____	1
	PATCH PANEL COPPER 48 PORT & CABLE MANAGER Brand: _____ Model: _____	9
	UPS - 11KVA Brand: _____ Model: _____	1
	BATTERY PACK FOR UPS Brand: _____ Model: _____	6

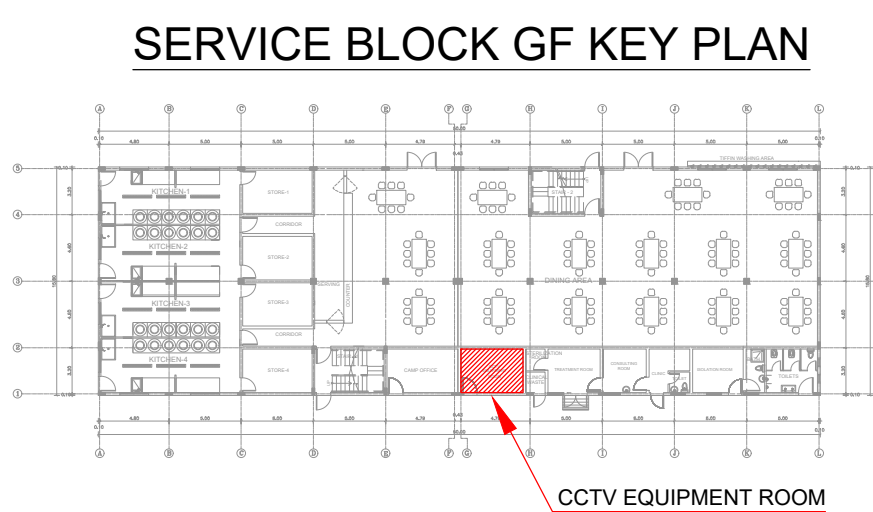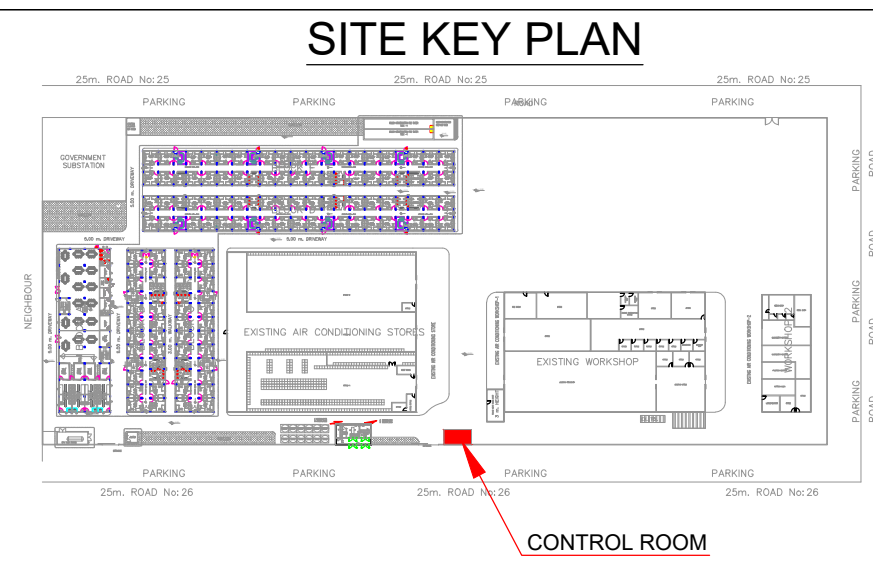

NOTES:

1. ALL DIMENSIONS ARE IN "METER" UNLESS OTHERWISE - STATED.
2. ALL CAMERAS ARE IP BASED AS PER SSD STANDARDS.
3. ALL CAMERAS MOUNTING HEIGHT SHOULD NOT BE - REACHABLE FROM FFL.
4. ANPR CAMERAS MOUNTING HEIGHT SHOULD NOT - EXCEED 1.3m FROM FFL.

REV.	DATE	DESCRIPTION	CHK	APVD
00	15/12/2025	ISSUED FOR SSD APPROVAL	***	***

CLIENT:

CCTV CONTRACTOR :

OWNER :
XXXXXXXXXXXXXXXXXXXXX
PROJECT NAME:
XXXXXXXXXXXXXXXXXXXXX
LOCATION : XXXXXXXXXX
STREET: XXXX ZONE: XX BUILDING: XXXXX
TITLE :
CCTV CONTROL ROOM & EQUIPMENT ROOM
DETAILED LAYOUT

DESIGNED : ***	APPROVED : ***
DRAWN BY : ***	
SCALE : AS SHOWN	PAPER SIZE : A1
PROJ. NO : ***	PIN. NO : ***
DATE : 15 DEC, 2025	SHEET NO : 1 OF 1
DRG. No : ABCD-CCTV-CR-02	REV : 00