



NEIGHBOR BUILDING

PLOT LIMIT

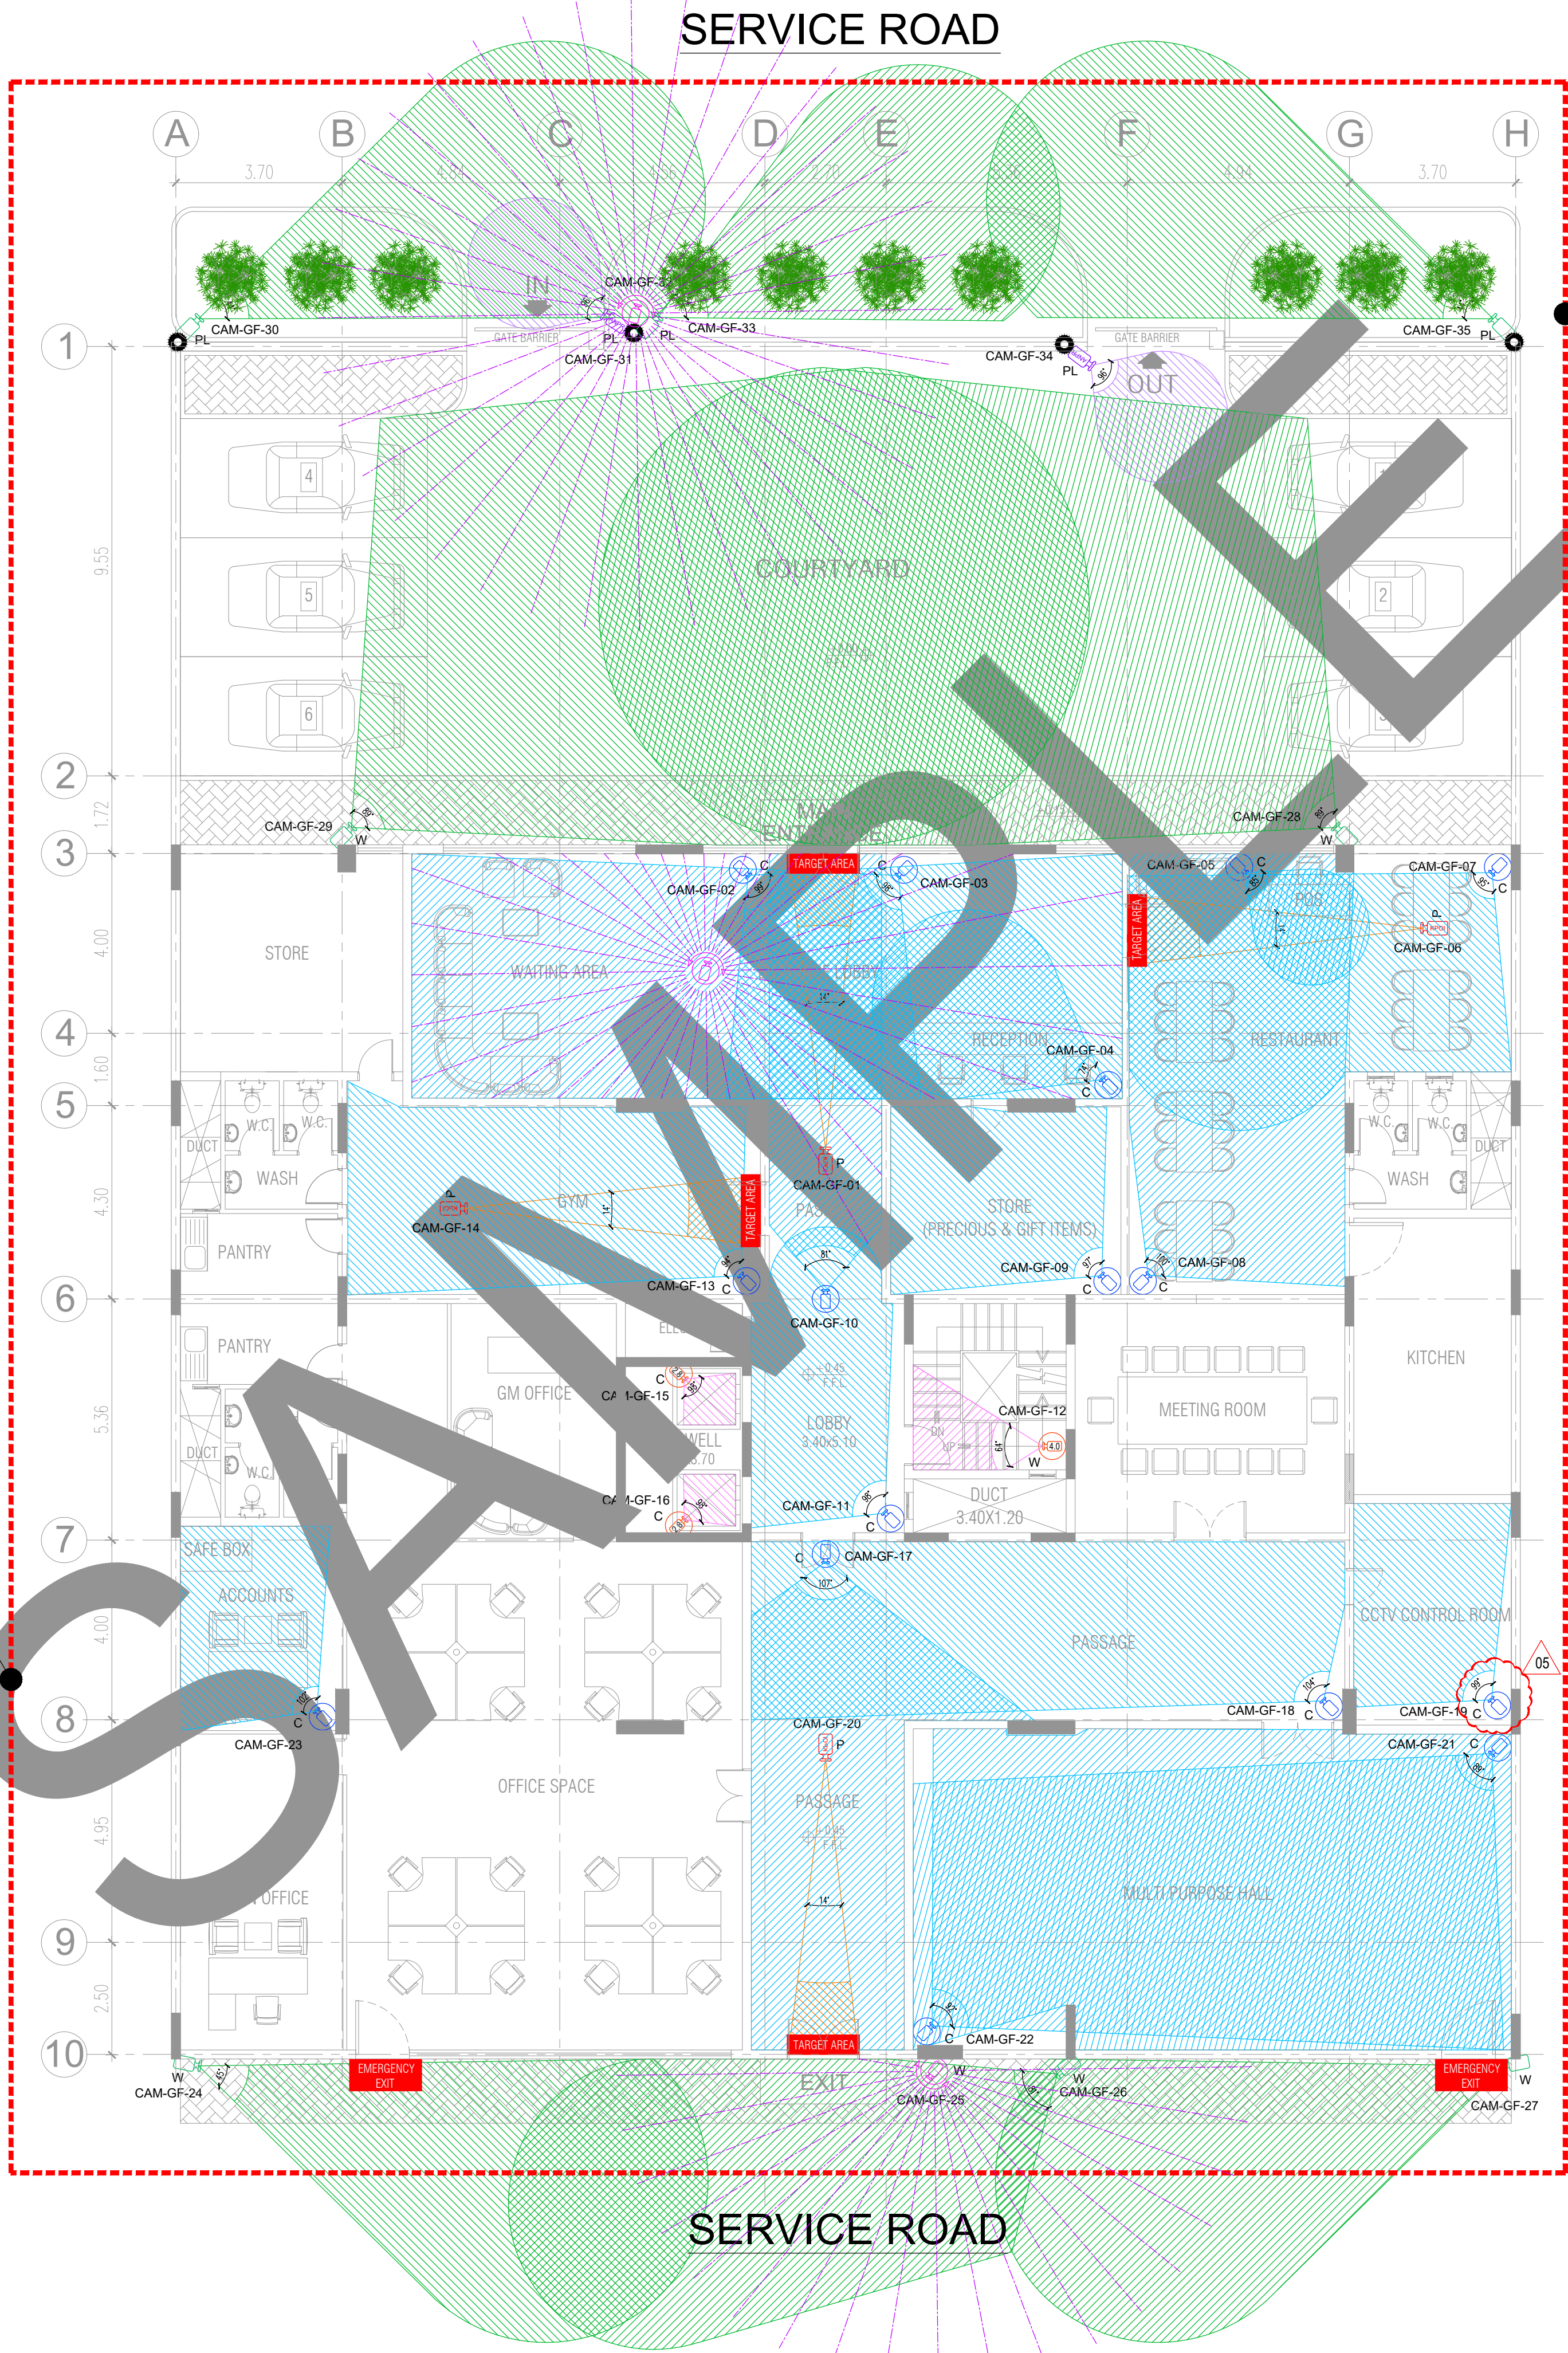

NEIGHBOR BUILDING

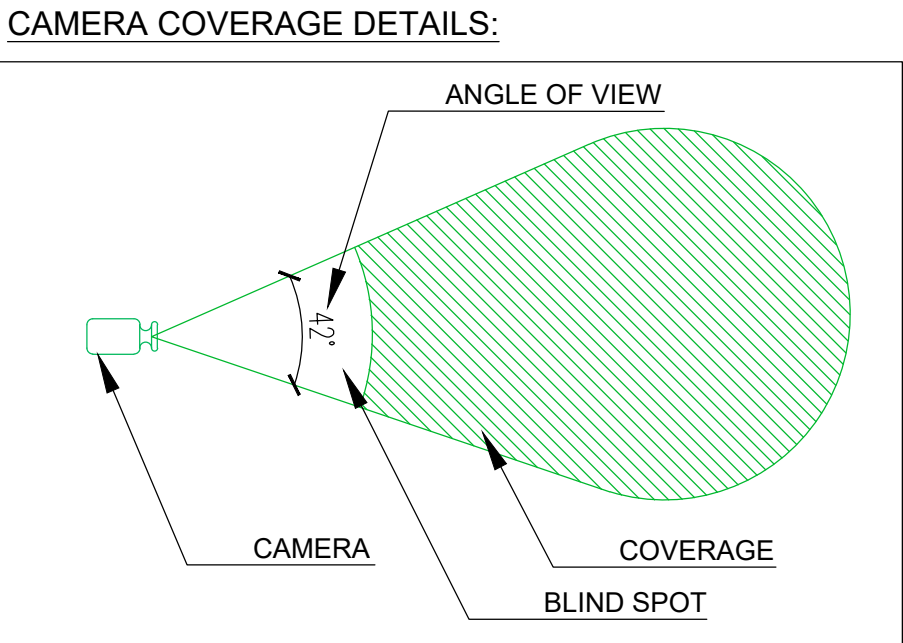


COLOR CODE (GENERAL):

DESCRIPTION	COLOR	LINE WEIGHT	LINE TYPE
Architectural plan	252	0.130mm	Straight
Grid & dimension	8	0.050mm	Center
Rev.cloud & notes	Red	0.150mm	Straight

REV. CLOUD 01

COLOR CODE (CCTV SYSTEM):


DESCRIPTION	SYMBOLS			FOV (COVERAGE)		
	COLOR	LINE WEIGHT	LINE TYPE	COLOR	LINE WEIGHT	LINE TYPE
Fixed Dome Camera	20	0.250mm	Straight	211	0.100mm	Straight
Verifocal Dome camera	160	0.250mm	Straight	140	0.100mm	Center
Fixed Bullet Camera	36	0.250mm	Straight	42	0.100mm	Straight
Verifocal Bullet Camera	114	0.250mm	Straight	104	0.100mm	Straight
PTZ Dome Camera	210	0.250mm	Straight	201	0.100mm	Straight
ANPR Box Camera	190	0.250mm	Straight	191	0.100mm	Straight
KPOI Box Camera	10	0.250mm	Straight	30	0.100mm	Straight
Camera Tag Number	7	0.130mm	Straight			
Title Block	7	0.130mm	Straight			
Title Block - Texts	7	0.130mm	Straight			
Title Block - Notes	7	0.130mm	Straight			
Key Plan	8	0.050mm	Straight			
Key Plan - Hatch	Red	0.150mm	Straight			

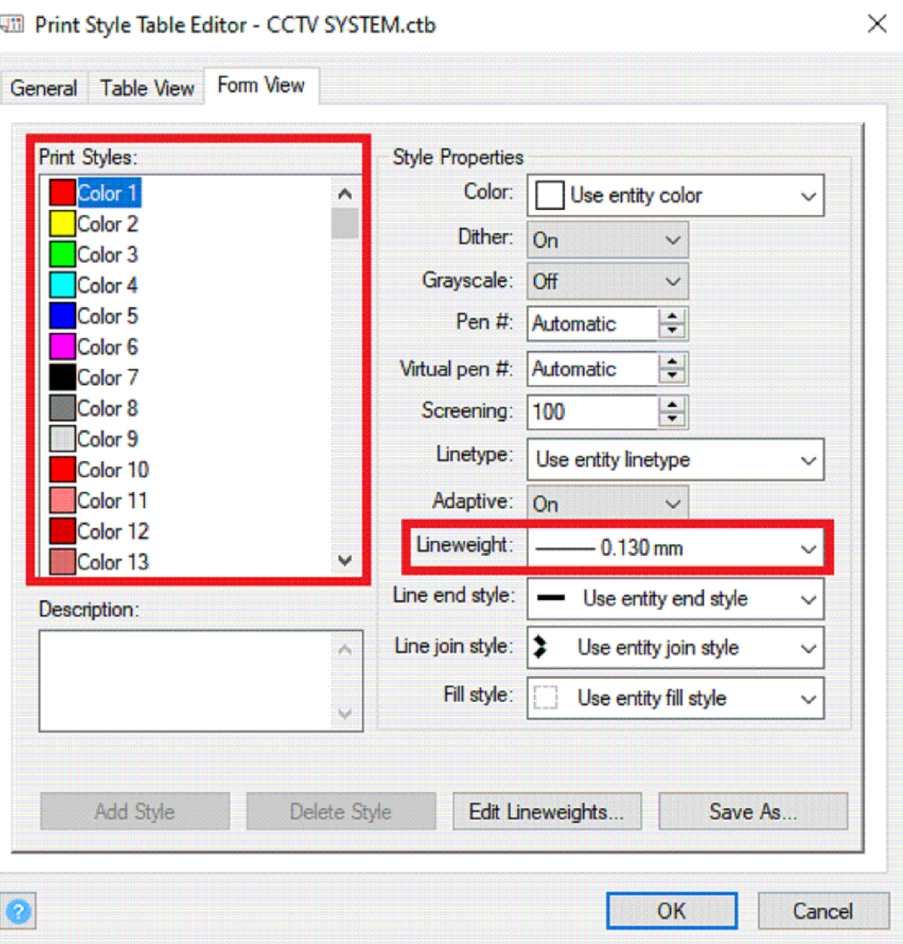

GUIDELINES FOR COLOR CODES USED IN THE DRAWINGS

FIELD OF VIEW TABLE (SAMPLE)

CAMERA MODEL	IDENTIFY	RECOGNIZE	OBSERVE	DETECTION
XX-XXX-XXXXXX	3.0 m	7.0 m	12.0 m	25.0 m
XX-XXX-XXXXXX	3.0 m	7.0 m	12.0 m	25.0 m
XX-XXX-XXXXXX	3.0 m	7.0 m	12.0 m	25.0 m
XX-XXX-XXXXXX	3.0 m	7.0 m	12.0 m	25.0 m

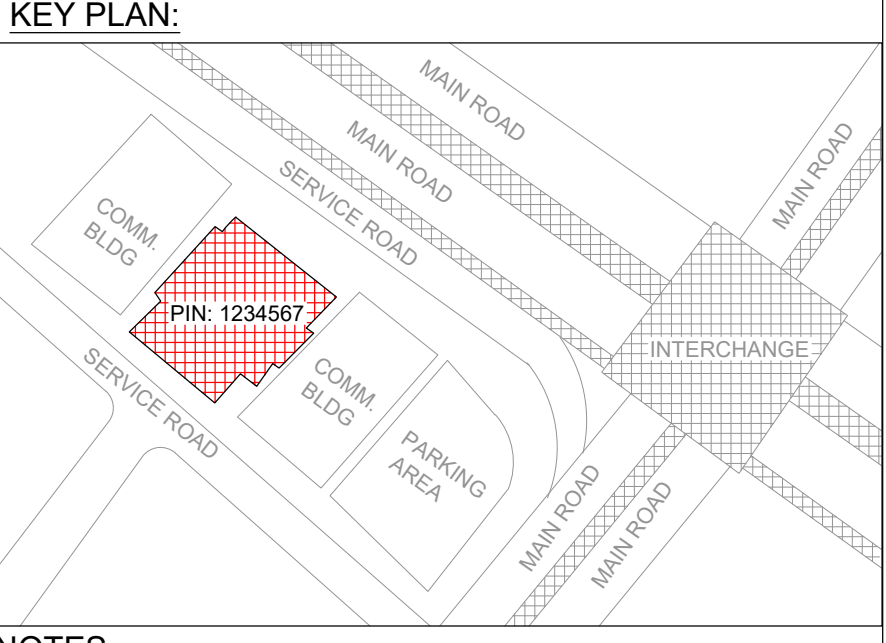

- NOTES:
1. ALL DIMENSIONS ARE IN "METER" UNLESS OTHERWISE STATED.
 2. ALL CAMERAS ARE IP BASED AS PER SSD STANDARDS.
 3. ALL CAMERAS MOUNTING HEIGHT SHOULD NOT BE REACHABLE FROM FFL.
 4. ANPR CAMERAS MOUNTING HEIGHT SHOULD NOT EXCEED 1.3m FROM FFL.
 5. NEW ADDITIONAL CAMERA.

LEGENDS:

SYMBOLS	DESCRIPTIONS	QTY
	2MP FIXED DOME CAMERA BRAND: _____, MODEL: _____	03
	2MP VERIFOCAL DOME CAMERA BRAND: _____, MODEL: _____	16
	2MP FIXED BULLET CAMERA BRAND: _____, MODEL: _____	00
	2MP VERIFOCAL BULLET CAMERA BRAND: _____, MODEL: _____	08
	2MP PTZ DOME CAMERA BRAND: _____, MODEL: _____	03
	2MP ANPR BOX CAMERA BRAND: _____, MODEL: _____	02
	4MP KPOI BOX CAMERA BRAND: _____, MODEL: _____	04
TOTAL NUMBER OF CAMERAS:		35

ABBREVIATION:

C = CEILING MOUNT, W = WALL MOUNT, P = PENDANT MOUNT
PL = POLE MOUNT

00	15/12/2025	ISSUED FOR SSD APPROVAL	***	***
REV.	DATE	DESCRIPTION	CHK	APVD
SCHEDULE OF REVISIONS				

CLIENT:

CCTV CONTRACTOR :

OWNER :
PROJECT NAME :
LOCATION :
STREET: XXXX ZONE: XX BUILDING: XXXX
TITLE :
GROUND FLOOR PLAN
CCTV SYSTEM LAYOUT

DESIGNED : ***	APPROVED : ***
DRAWN BY : ***	
SCALE : 1:100	PAPER SIZE : A1
PROJ. NO : ***	PIN. NO : ***
DATE : 15 DEC, 2025	SHEET NO : 1 OF 1
DRG. No : ABCD-CCTV-GF-01	REV : 00